

Date: DEC.01.2024 Scales: AS SHOWN

Drawn by: F.T.

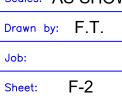

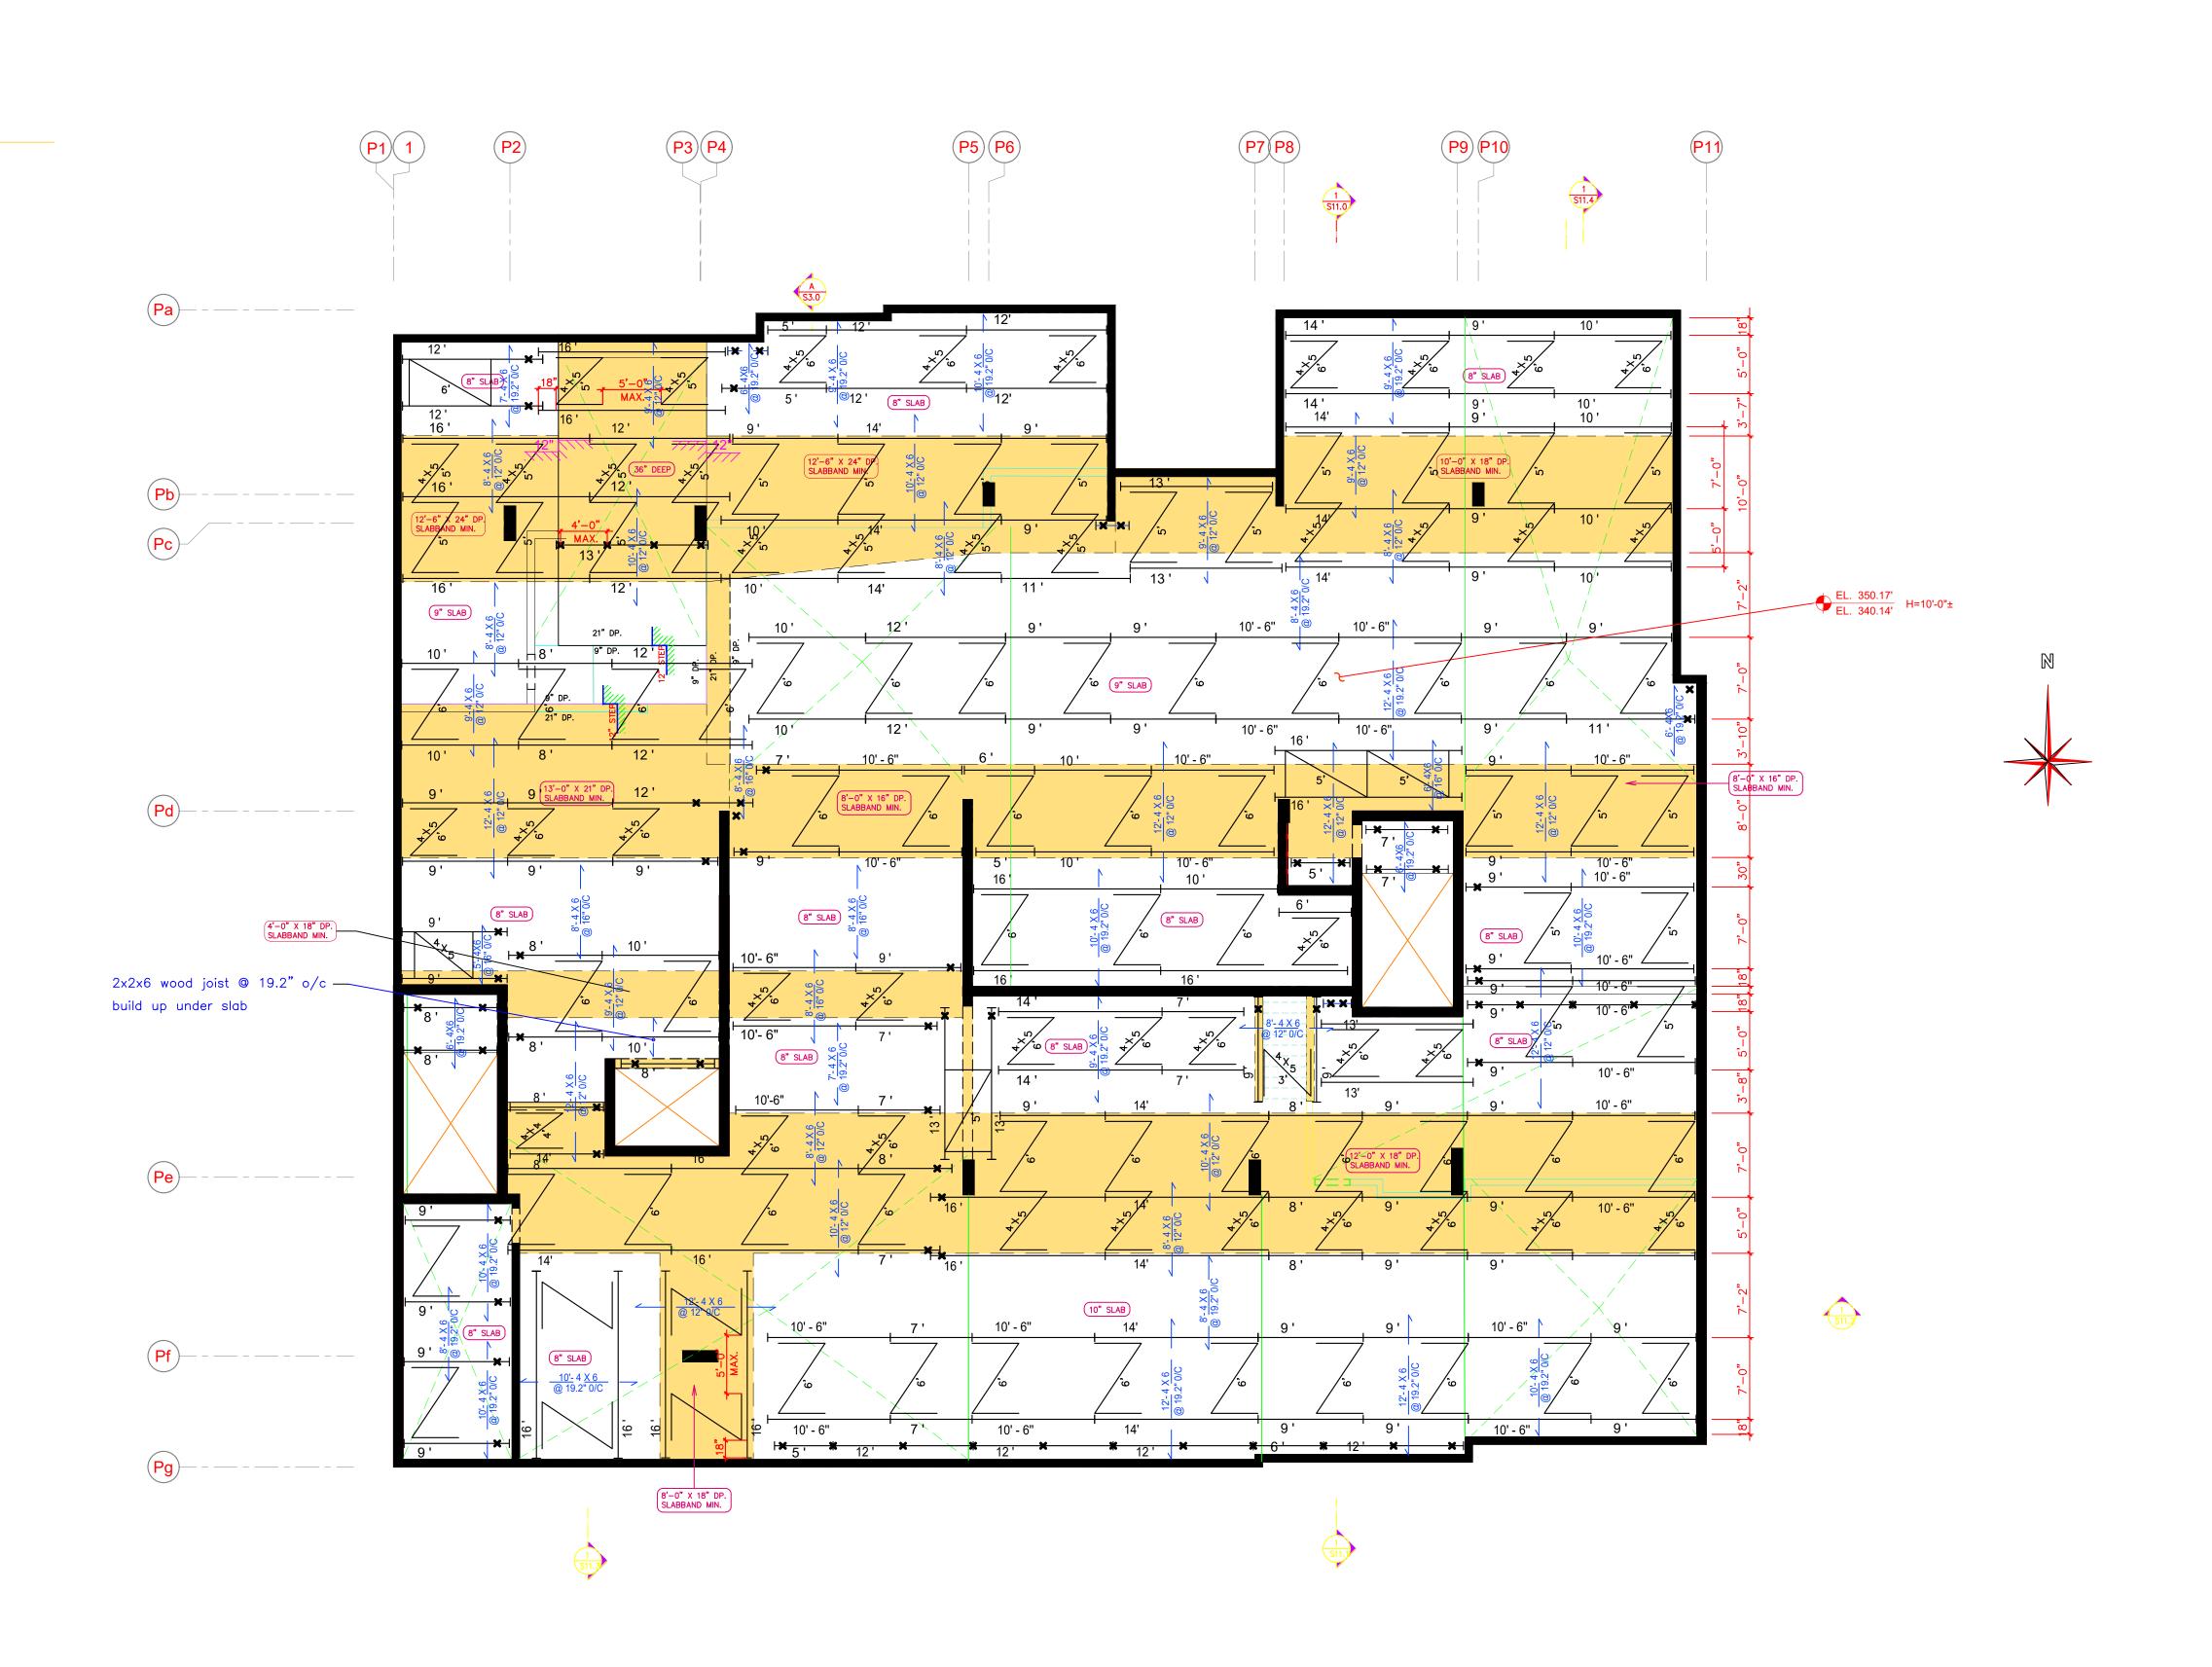

NOTES:

THIS DRAWING SHALL BE READ IN CONJUNCTION WITH ARCHITECTURAL AND STRUCTURAL DRAWINGS.

" \leftarrow -" DENOTES AS 2X2X6 WOOD JOISTS SHORTER THAN 5'-0" LONG TYP.

CONTRACTOR TO CHECK AND CONFIRM ALL DIMENSIONS & ELEVATIONS PRIOR TO SHIPMENT OF EQUIPMENT.

PARKING LEVEL P1 SUSPENDED SLAB SHORING PLAN: SCALE 1/8"=1'-0"

(150 P.S.F.) 8" DEEP SLAB TYPICAL U.N.O. 18" DEEP SLAB BAND TYPICAL U.N.O. (275 P.S.F.)

ALL FRAMES TO BE 4' WIDE HEAVY DUTY(10 K/LEG) WITH 7'-0" BRACING TYP. (SEE PLAN FOR THE HEIGHT). NO SHORE IS REQUIRED UNDER SLAB TYP. UNLESS SHOWN OR MARKED AS "X" FOR #2 POST SHORE

PLYWOOD TO BE MIN. 3/4" D. FIR #1 OR BETTER.

4X6 WOOD JOISTS SUPPLIED BY TTF SCAFFOLDING SHALL NOT BE USED FOR PACKING

OR CUT SHORT FOR OTHER PURPOSES.

FOR GENERAL NOTES AND TYPICAL DETAILS SEE DRAWING F-1.

(48 HOURS NOTICE PLEASE).

INSPECTION IS REQUIRED BY UNDERSIGNED P. ENG. PRIOR TO POURING CONCRETE.